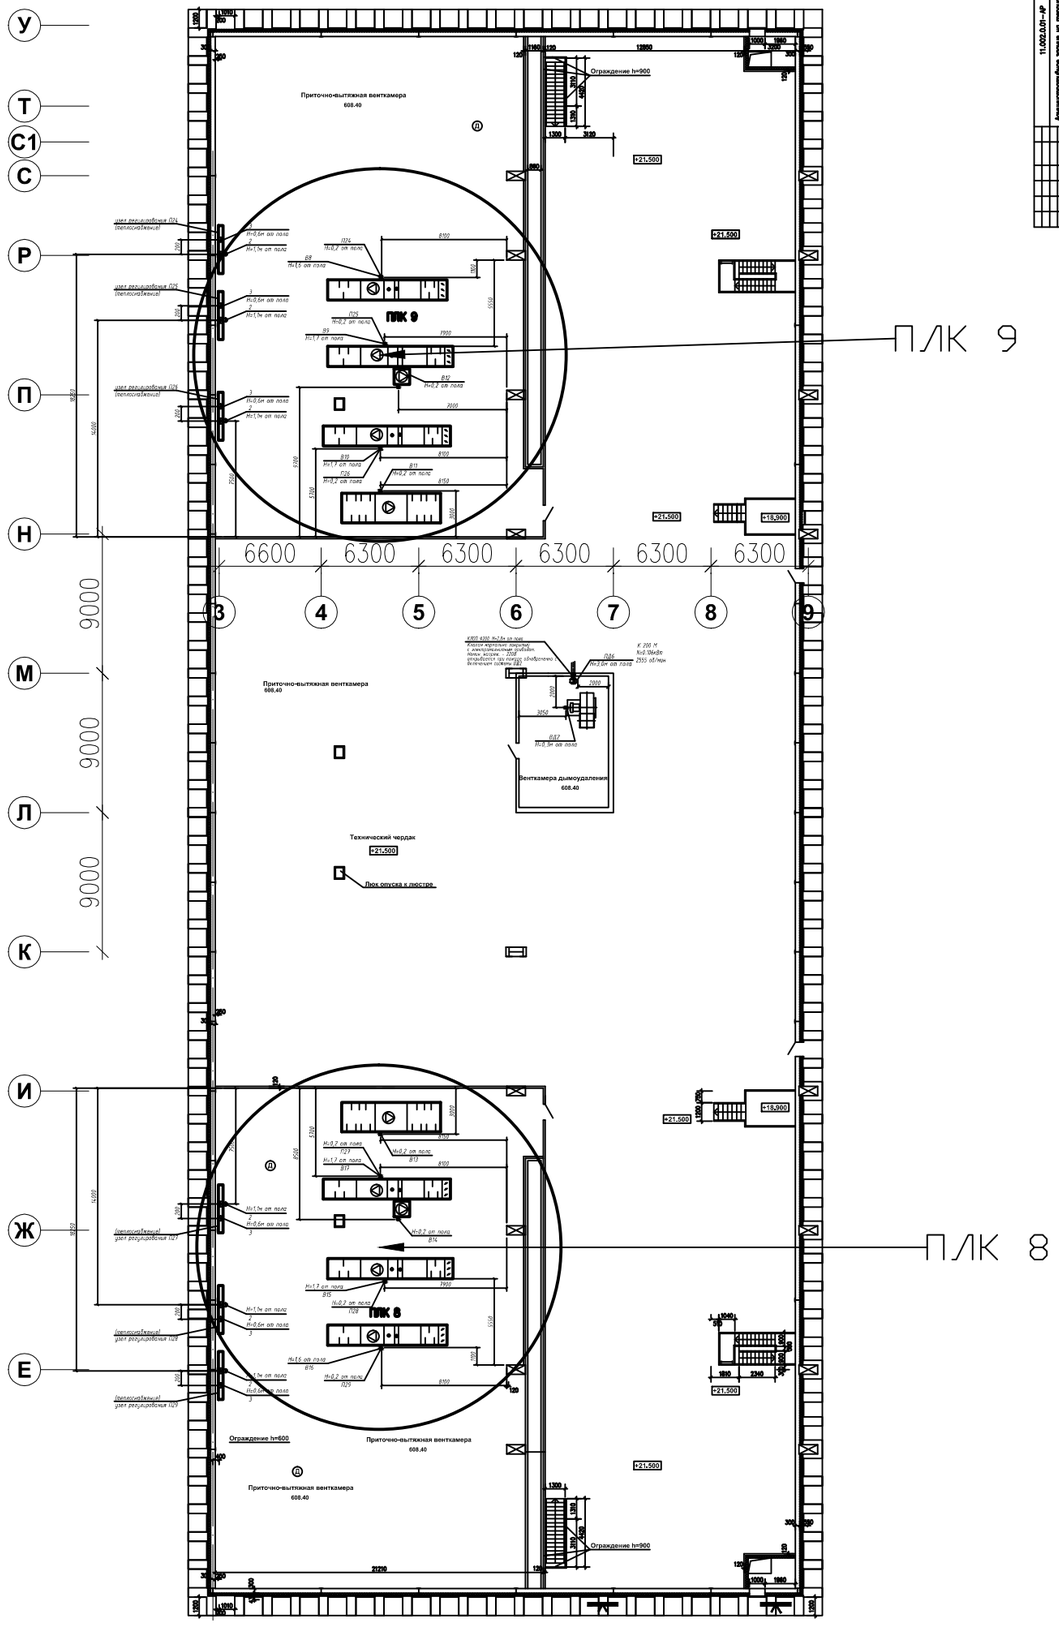
ПЛК 9
ПЛК 8
Приточно-вытяжная венткамера
608.40
Венткамера дымоудаления
608.40
Технический чердак
+21,500
+18,900
Ограждение h=900
Ограждение h=600
Люк откоса к люстре
6600
6300
9000
21750